

ELECTRICAL & CEILING PLAN  
SCALE:  $\frac{1}{4}$ " = 1'-0"

LEGEND:

- S SINGLE SWITCH
- S2 TWO WAY SWITCH
- WP WATER PROOF OUTLET
- CFC1 BATHROOM OUTLET
- DU DUPLEX OUTLET
- DB DOOR BELL
- SP SPEAKER
- WP WATER PROOF SPEAKER
- CEILING MOUNTED LIGHT
- PENDANT LIGHT
- TABLE LAMP
- FLOOR LAMP
- WALL MOUNTED LIGHT
- UNDER CABINET LIGHT
- WALL MOUNTED TRACE LIGHT
- SHELVING LIGHTING


PROJECT: SHERMAN RESIDENCE  
DATE: [REDACTED]  
REVISION: [REDACTED]


SHEET NO:  
2



COLOR PLAN  
SCALE:  $\frac{1}{4}$ " = 1'-0"

PROJECT: SHERMAN RESIDENCE  
SHEET NO.: 3  
DATE: \_\_\_\_\_  
REVISION: \_\_\_\_\_

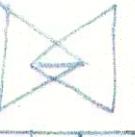

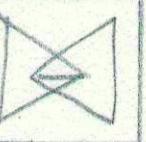


PROJECT: SHERMAN RESIDENCE

DATE: REVISION:


SHEET NO:

4

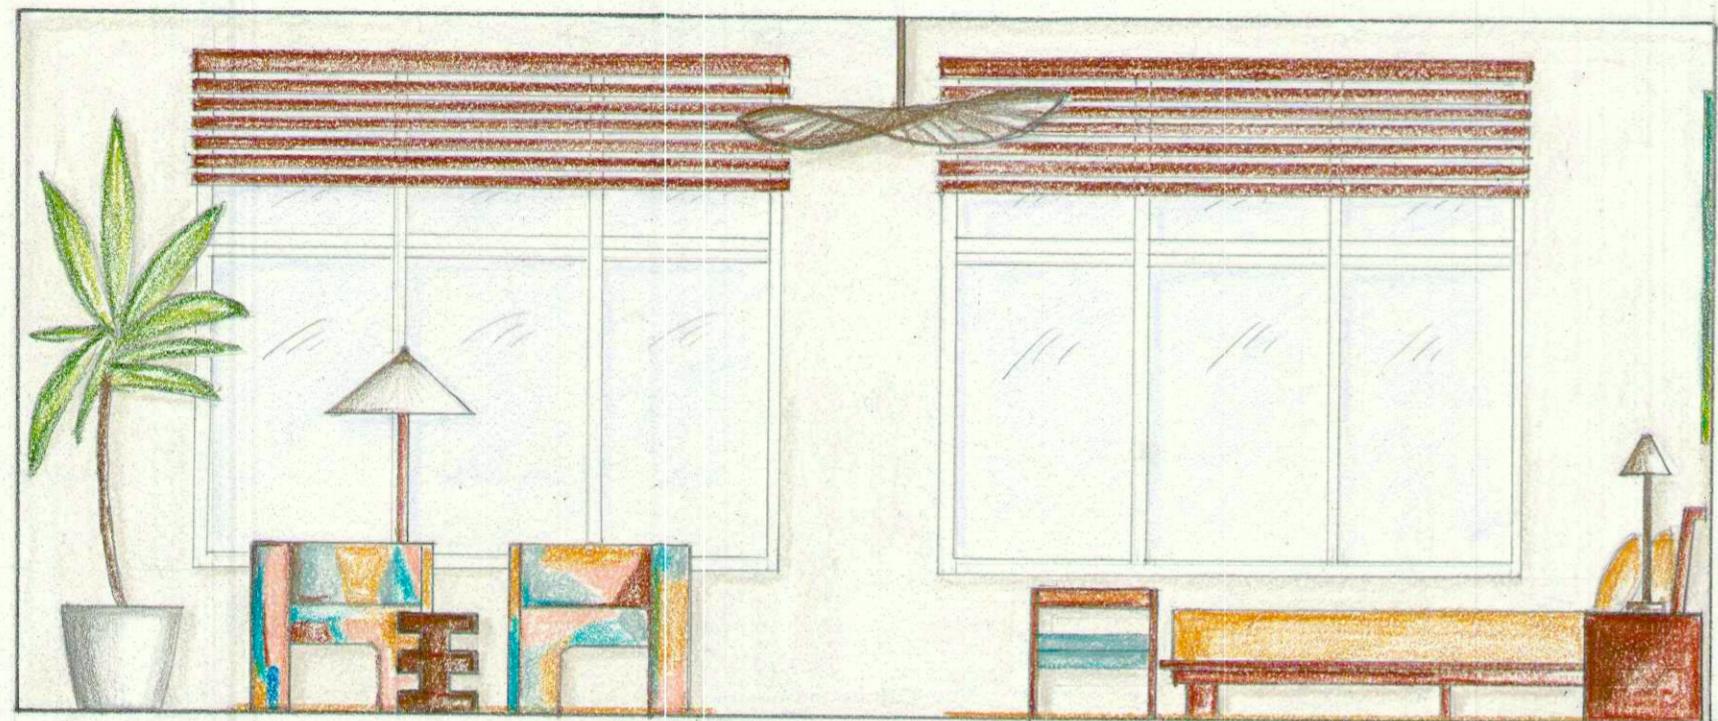


ELEVATION  
SCALE:  $\frac{3}{8}'' = 1'-0''$

(A)

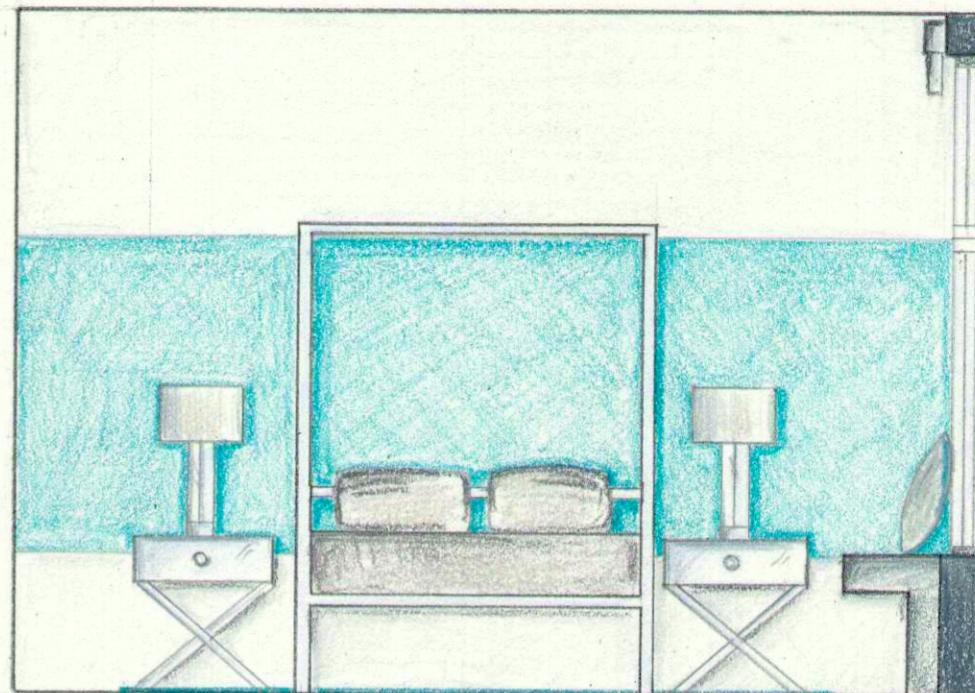


ELEVATION  
SCALE:  $\frac{3}{8}'' = 1'-0''$

(B)

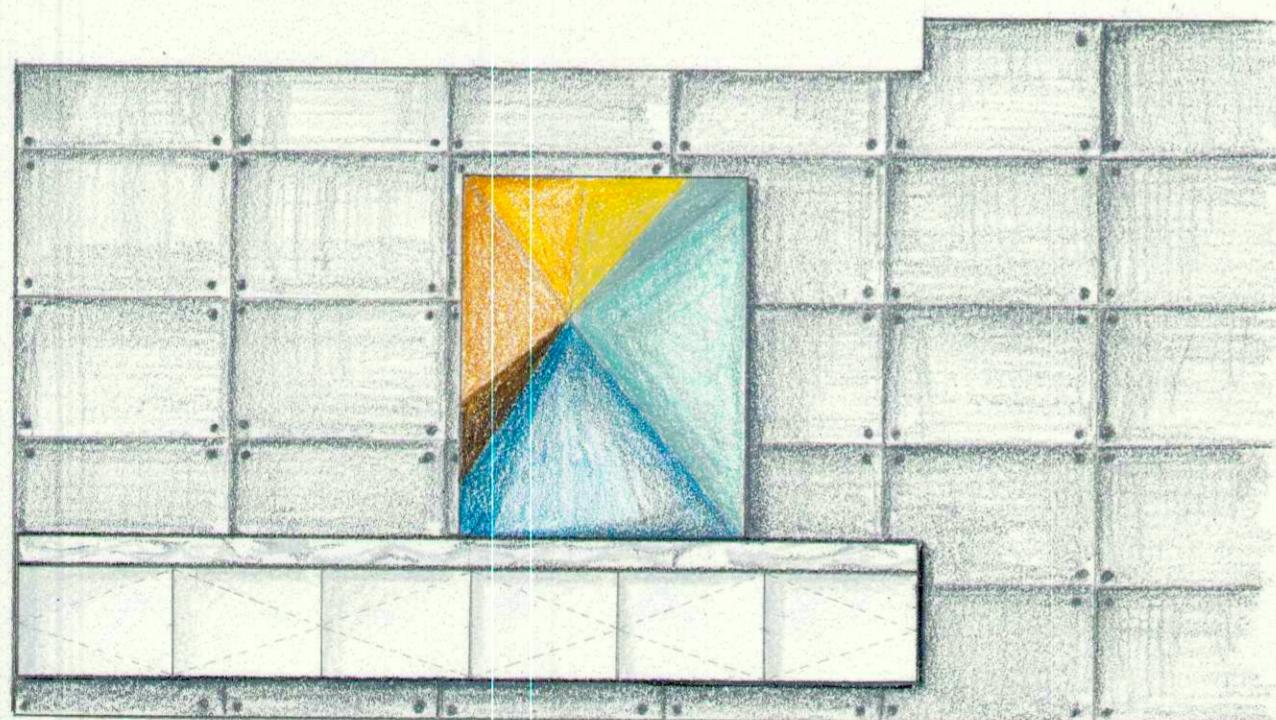


ELEVATION  
SCALE:  $\frac{3}{8}'' = 1'-0''$

(C)

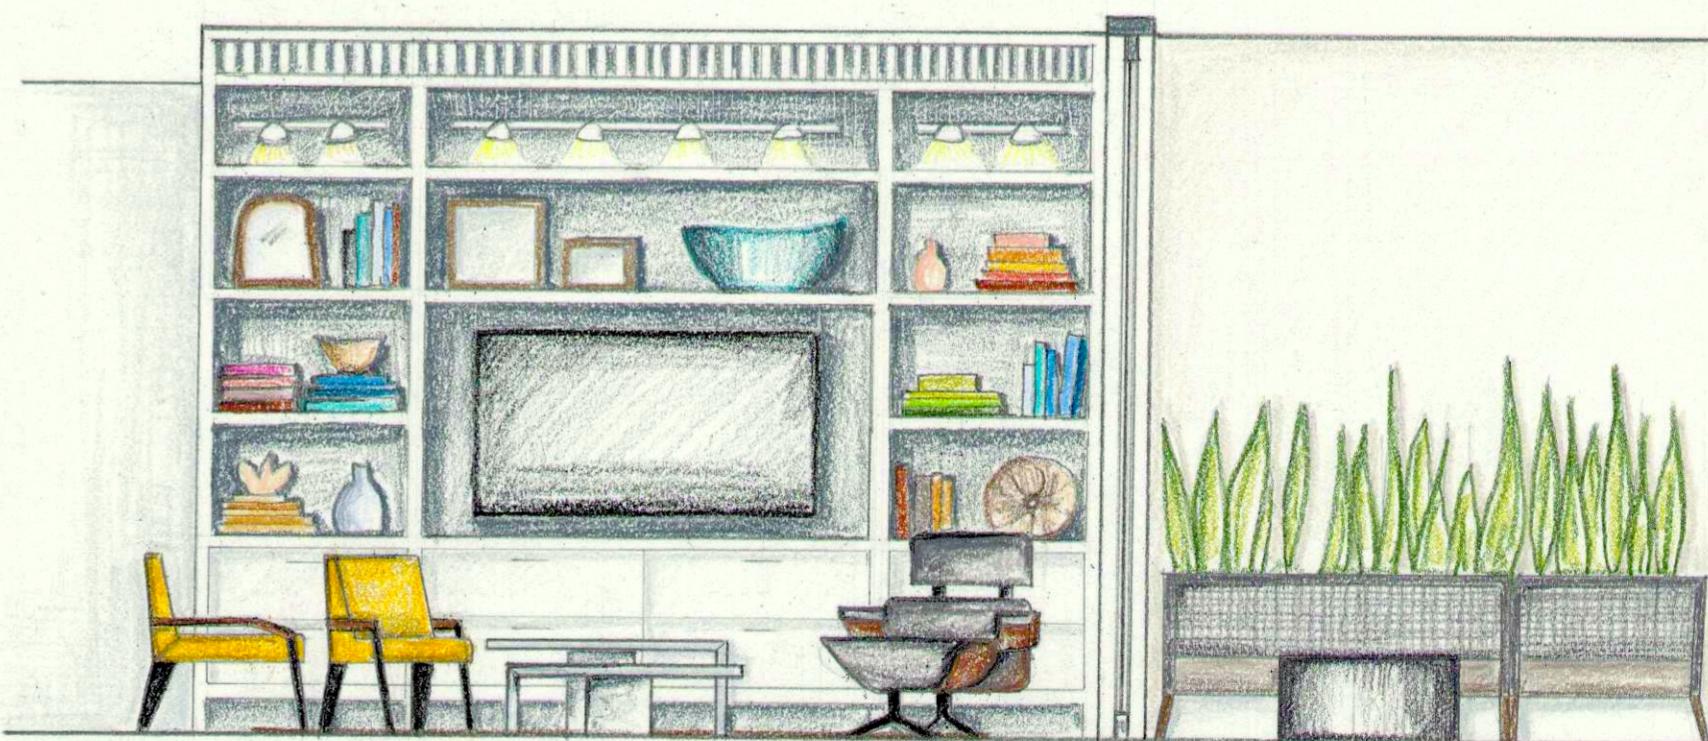

ELEVATION  
SCALE:  $\frac{3}{8}'' = 1'-0''$


(D)

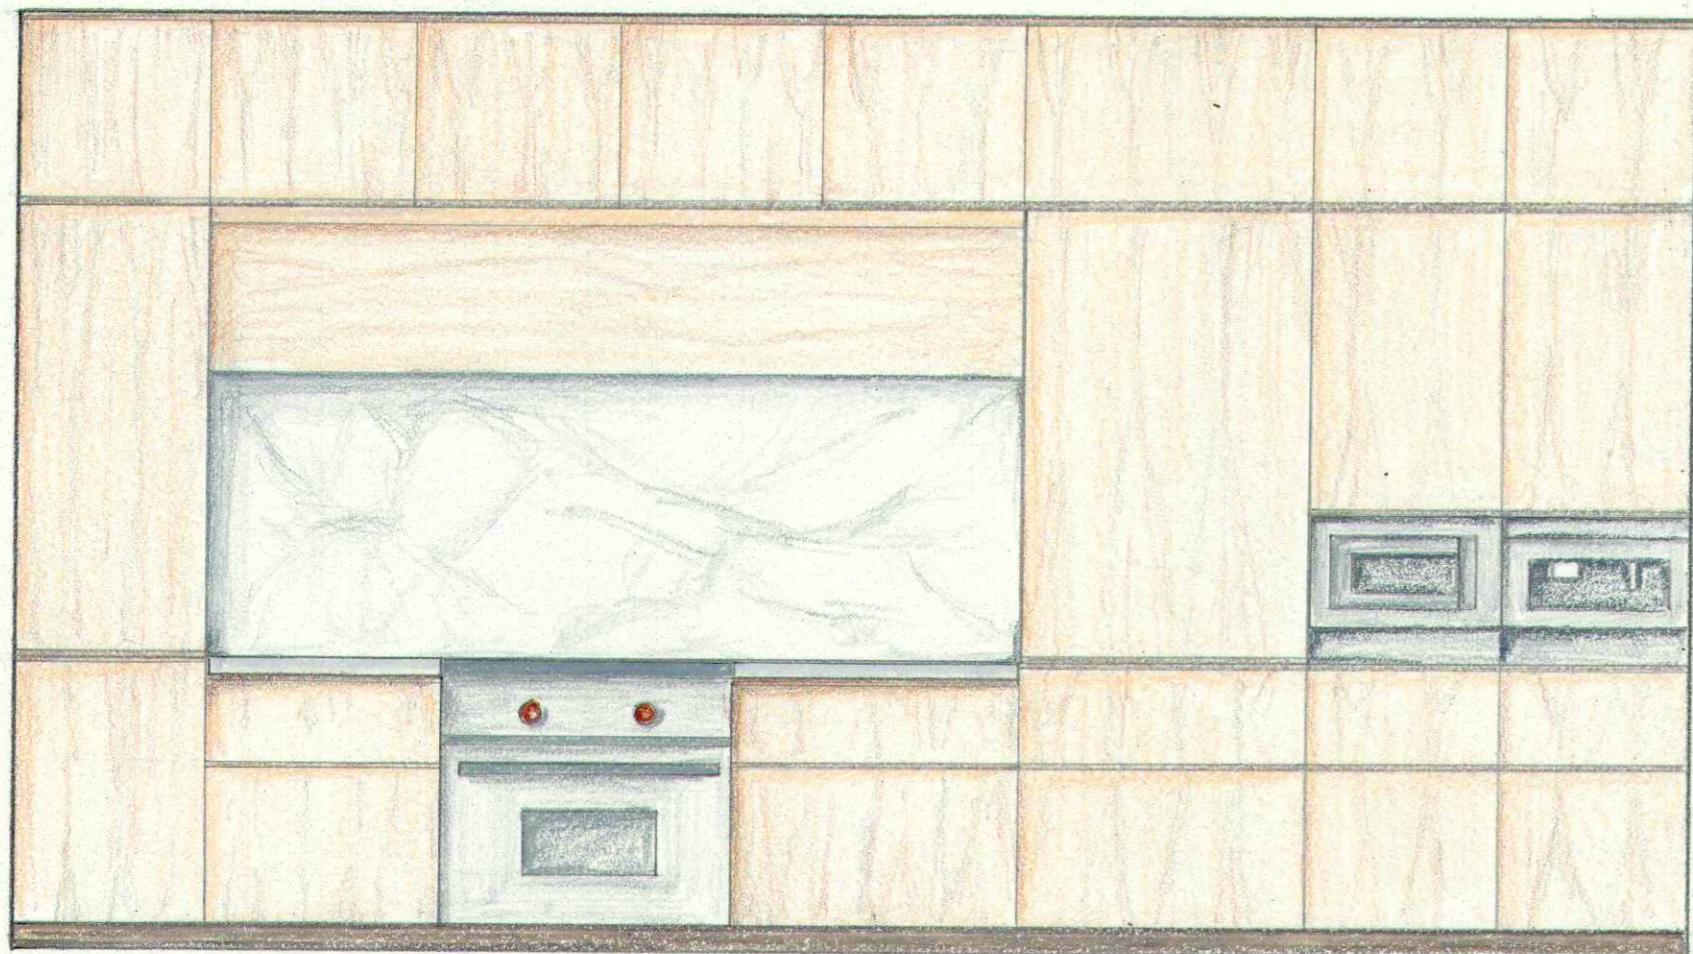

ELEVATION

SCALE :  $\frac{1}{2}$ " = 1'-0"

(E)

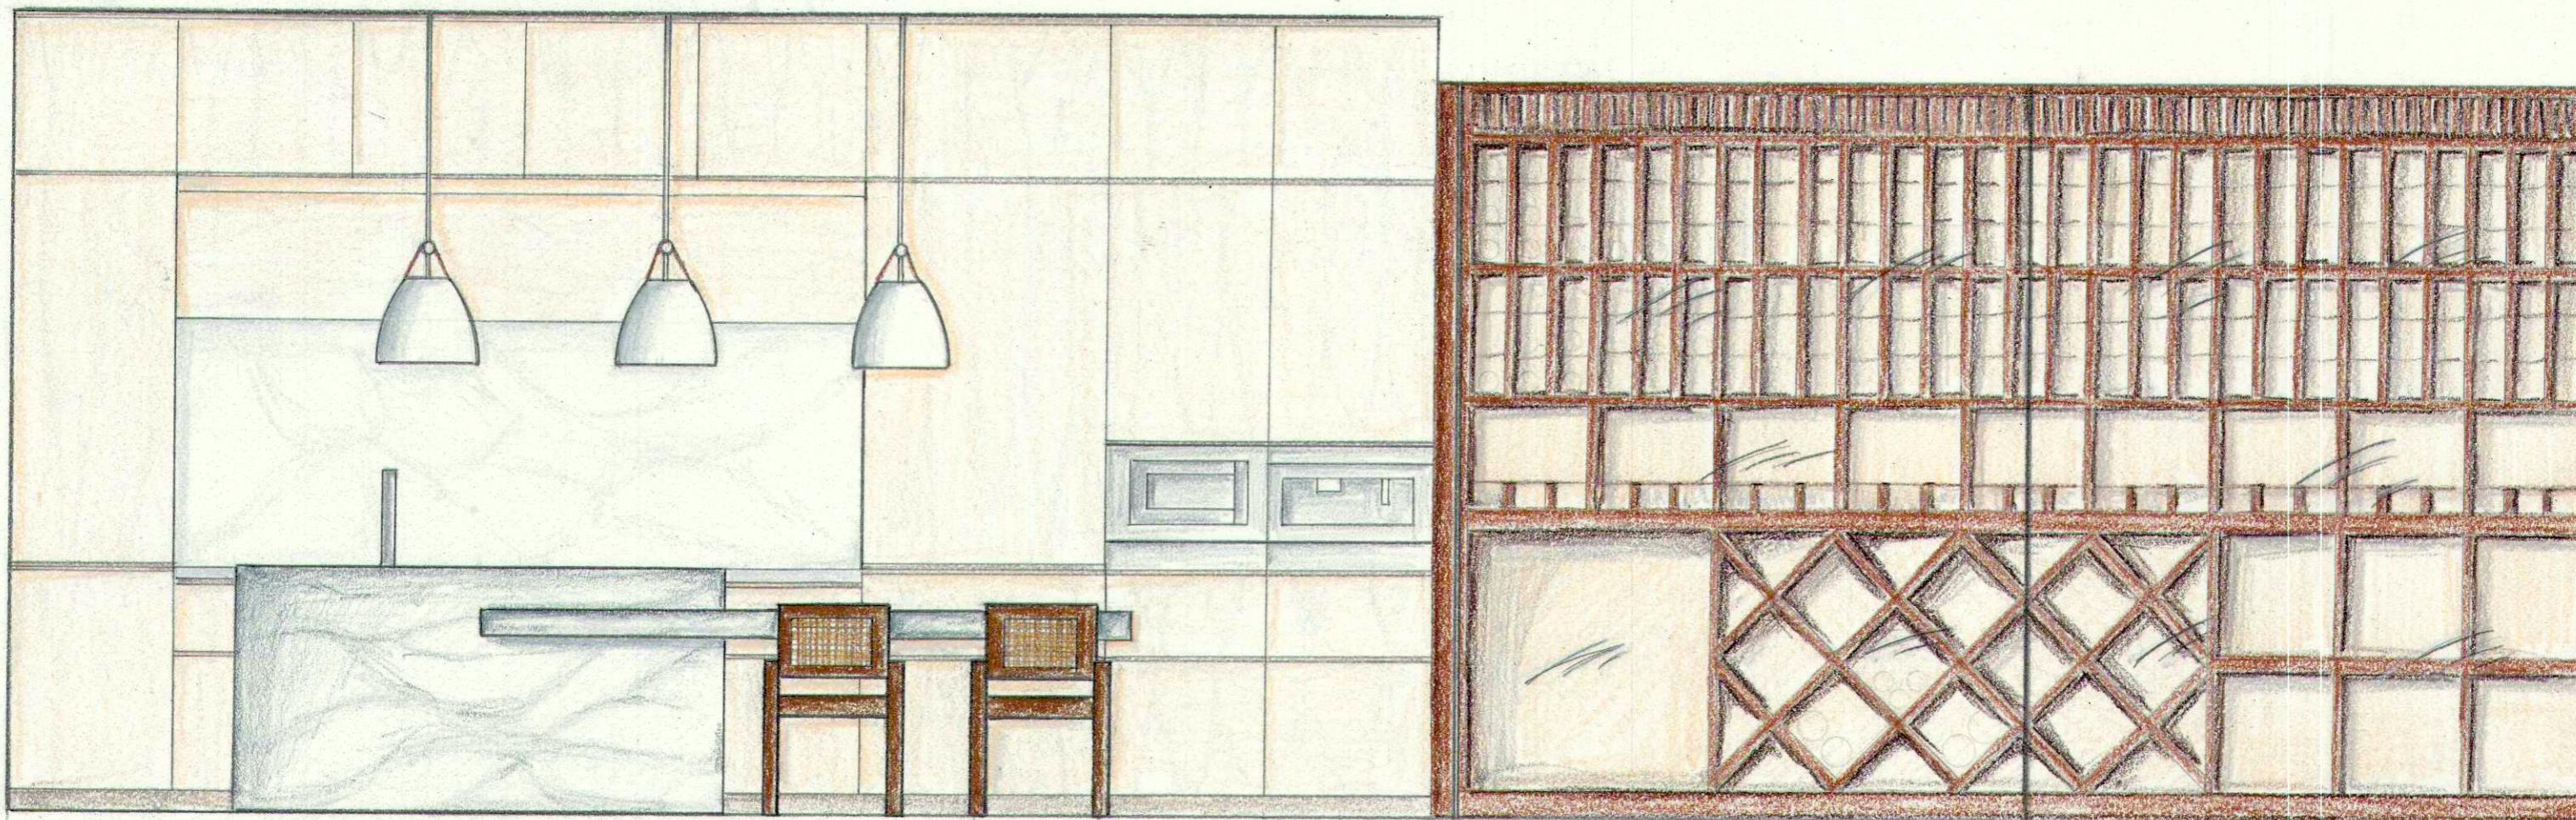

ELEVATION

SCALE :  $\frac{1}{2}$ " = 1'-0"

(F)

PROJECT: SHERMAN RESIDENCE

REVISION:

SHEET NO:

51

DATE: